

# Vista general

Distribución de la tienda · República Dominicana



# Panorámica desde la entrada

Vista de acceso hacia las áreas comerciales y el fondo de la tienda.



# Góndolas y pasillos

Exhibición central, cabeceras de producto y circulación comercial.



# Licores

Mueble con divisiones, identidad AM:PM y marco con acabado tipo ladrillo.



# Bebidas y Beer Cave

Frente refrigerado y acceso al Beer Cave desde el área de ventas.



# Food Service

Seis módulos iguales con productos reales; estación de hot dog con salsas y bandejas.



# Cajas y servicios

Dos cajas de venta y Mi Ban-kito, con pantallas orientadas al cliente.



# Café, panadería y refrigerado


Café de autoservicio, dos basureros integrados y alimentos listos para llevar.



# Terraza

Terraza de 25,05 m<sup>2</sup> con siete mesas compactas y centros de mesa.



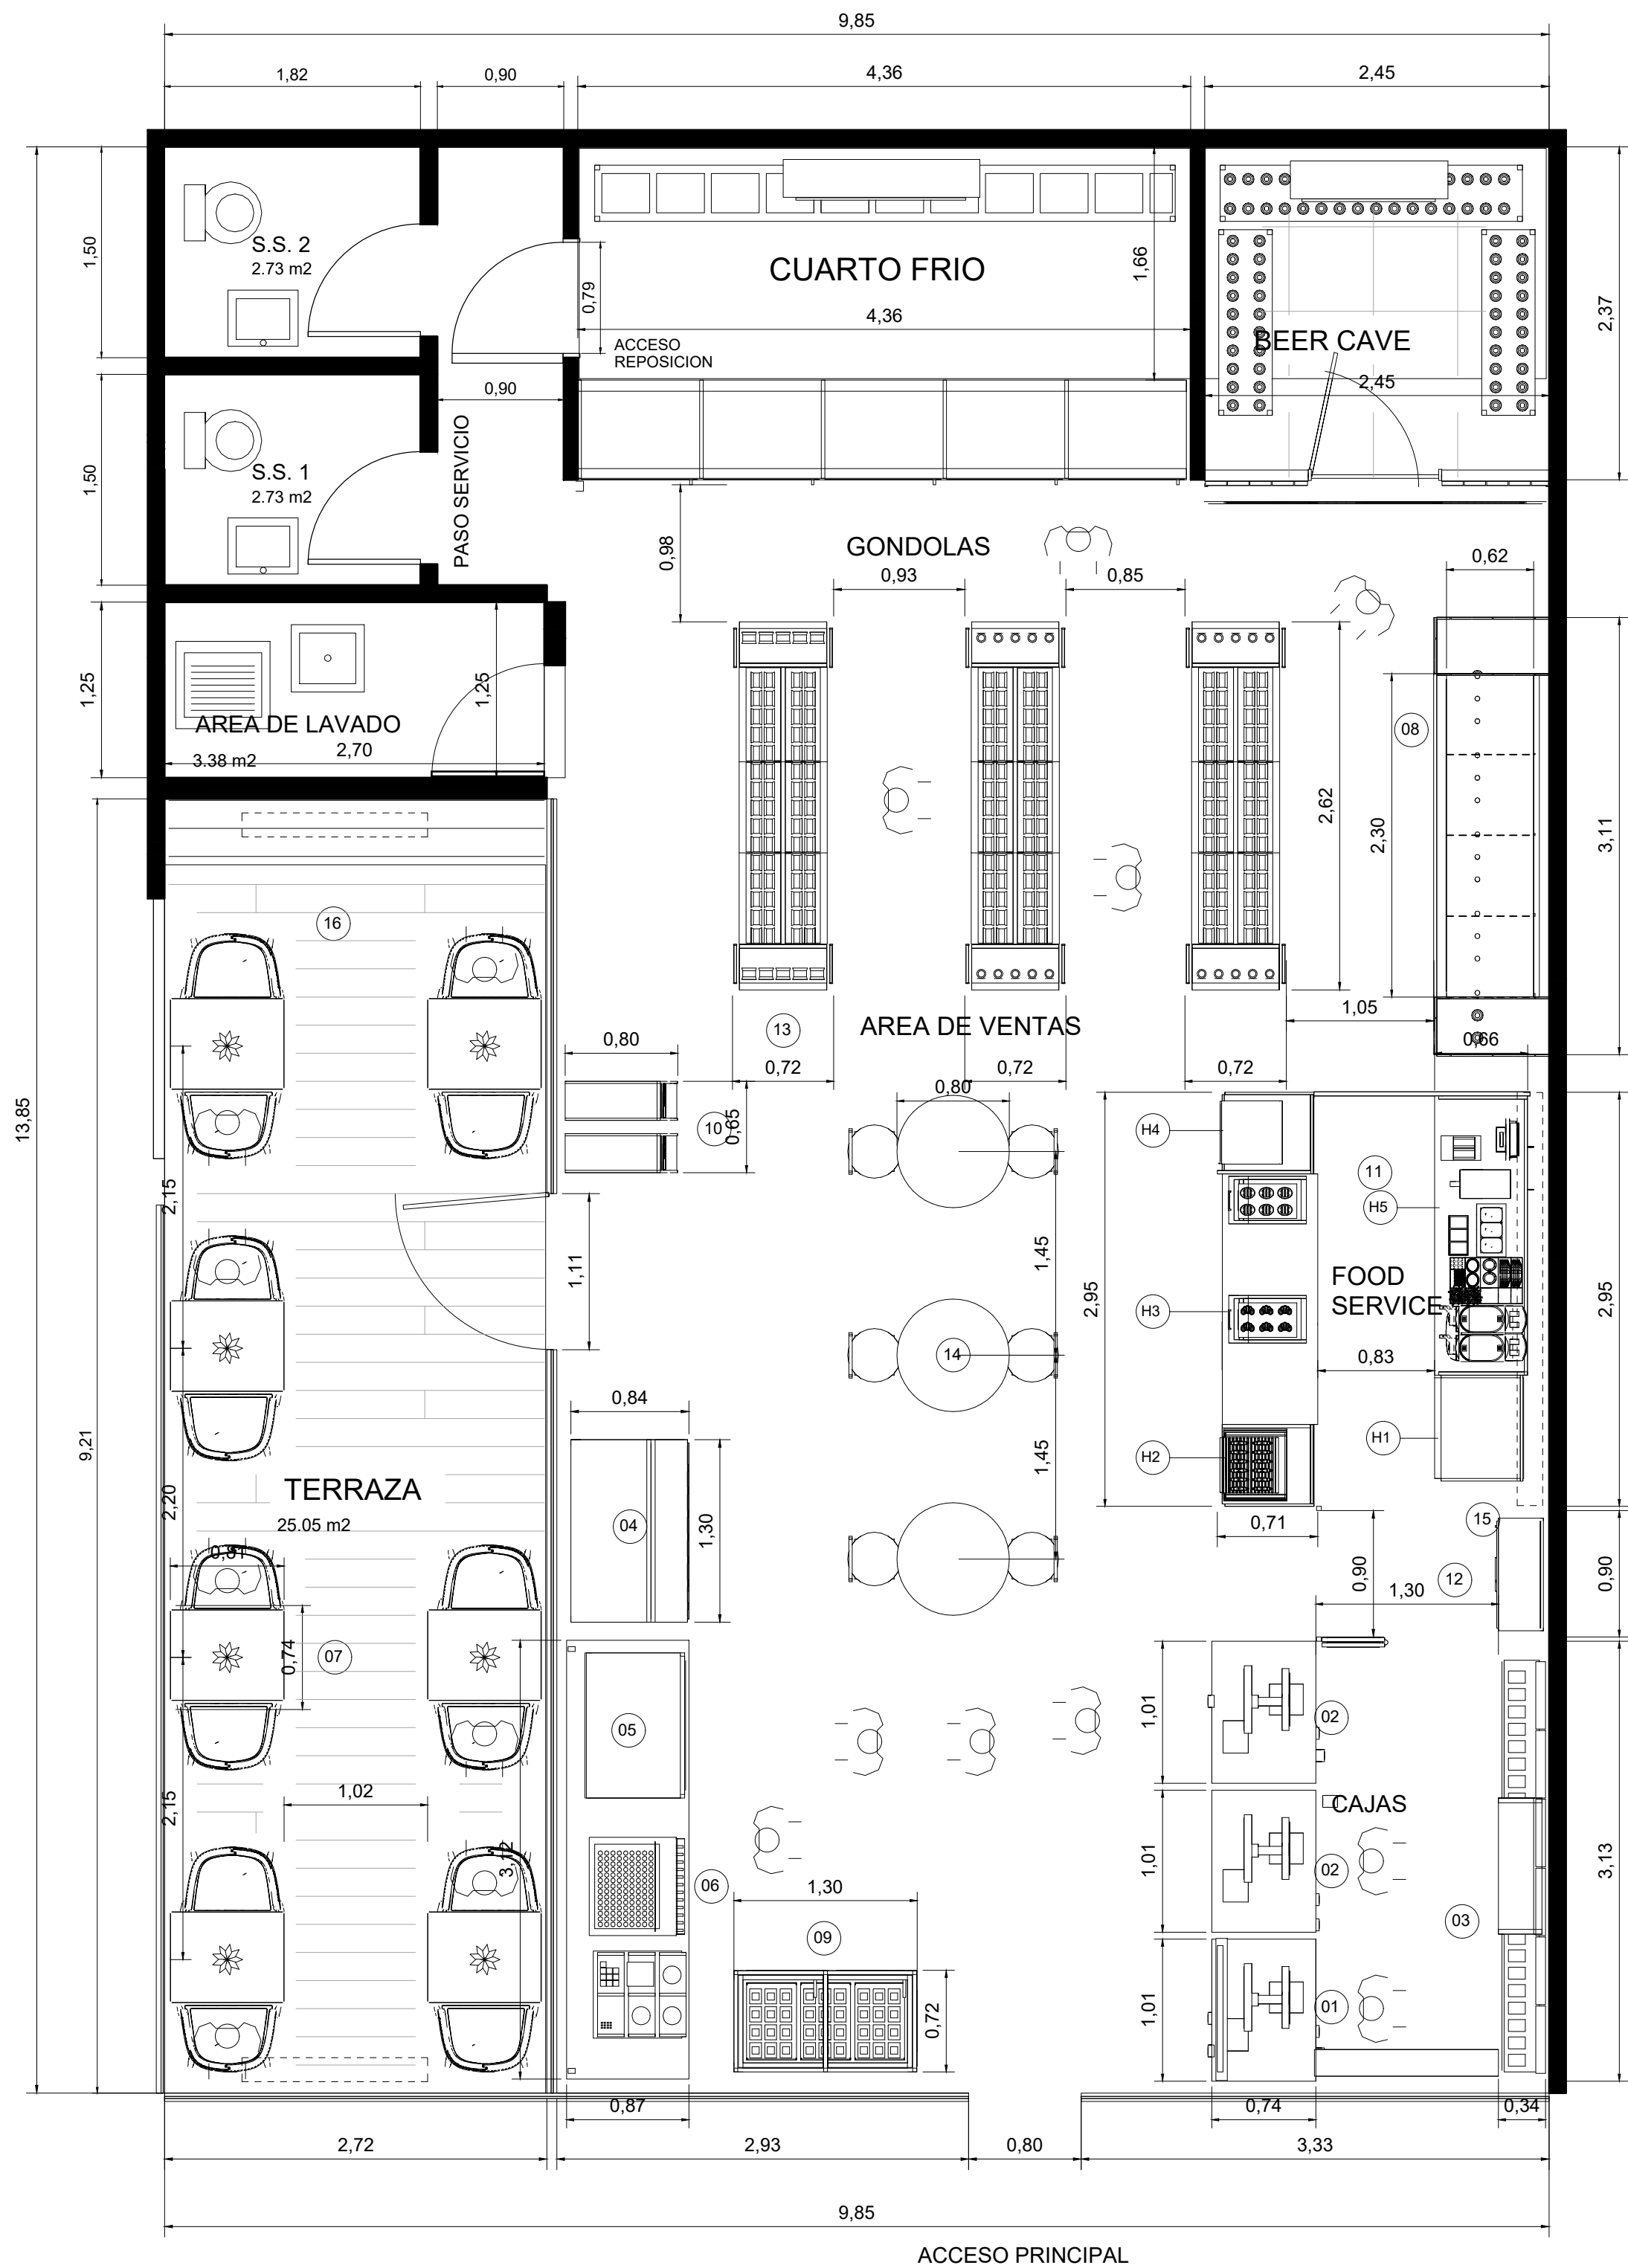

SIMBOLOGIA CONSTRUCTIVA

- Muros y tabiques en corte
- Mobiliario y equipamiento
- Vidrio / cerramiento ligero

Pisos: terraza / Beer Cave. Figuras humanas: escala y uso.

CUADRO DE EQUIPAMIENTO

| CLAVE | DESCRIPCION                                | CANT. |
|-------|--------------------------------------------|-------|
| 01    | Caja Mi Ban-kito / pagos y servicios       | 1     |
| 02    | Caja normal con exhibicion de productos    | 2     |
| 03    | Backwall / modulo central de cigarros      | 1     |
| 04    | Matahambritas: 1.30 x 0.84 x 2.20 m        | 1     |
| 05    | Vitrina de panaderia: frente 1.032 m       | 1     |
| 06    | Cafetera + organizador de vasos            | 1     |
| 07    | Mesa compacta 0.81 x 0.74 m / terraza      | 7     |
| 08    | Mueble de licores / marco tipo ladrillo    | 1     |
| 09    | Paletero horizontal Helados Bon            | 1     |
| 10    | Cajero automatico ATM                      | 1     |
| 11    | Food Service: grill + 2 vitrinas acrilicas | 1     |
| 12    | Vitrina de electronica con vidrio          | 1     |
| 13    | Gondolas centrales: 0.72 x 2.62 m          | 3     |
| 14    | Mesa circular / alineada en area central   | 3     |
| 15    | Pantallas 55 pulgadas / Food Service       | 2     |
| 16    | Pantallas para ambiente musical / terraza  | 2     |

CUADRO DE SUPERFICIES / m2


| SECTOR                     | MEDIDAS / m     | m2    |
|----------------------------|-----------------|-------|
| Tienda y circulaciones (*) | Por diferencia  | 86,40 |
| Banos (2)                  | 2 x 1.82 x 1.50 | 5,46  |
| Terraza                    | 2.72 x 9.21     | 25,05 |
| Area de lavado             | 2.70 x 1.25     | 3,38  |
| Cuarto frio                | 4.36 x 2.37     | 10,33 |
| Beer Cave                  | 2.45 x 2.37     | 5,81  |

TOTAL INTERIOR DEL LOCAL 9.85 x 13.85 136,42

(\*) Incluye tabiques y pasos. No equivale a area util libre.  
Areas nominales del modelo; sin deducir muebles. Verificar en sitio.  
Paso 0.90 m con puerta fria cerrada; apertura hacia afuera.


D01 / LICORES - PLANTA DE MODULACION 1:20

Divisiones bajo repisa superior: linea discontinua en planta.

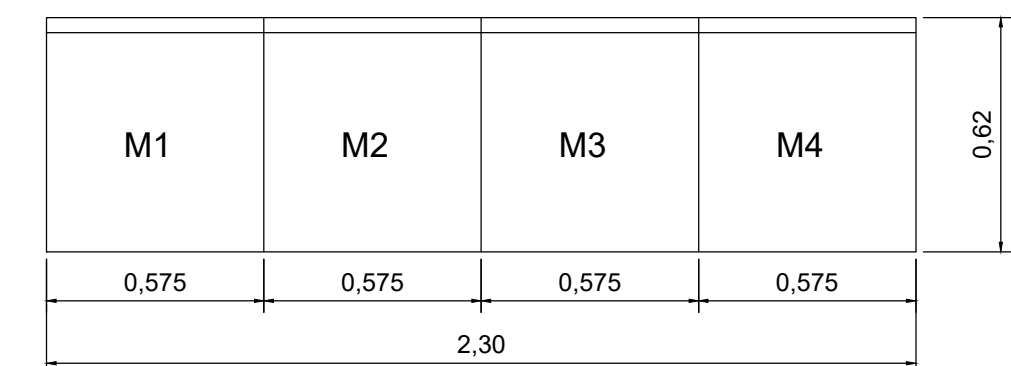

4 modulos nominales de 0.575 m / frente total 2.30 m.  
Fondo de repisas 0.62 m. Remates exteriores: 3.11 m total.  
Cotas del modelo. Espesores y medidas finales: verificar en sitio.

ESCALA GRAFICA / METROS

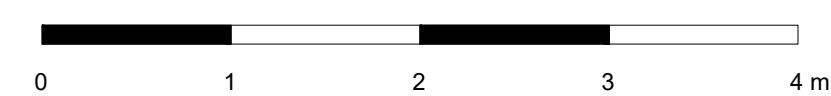

PLANTA ARQUITECTONICA  
TIENDA AM:PM / LOCAL 133



PROYECTO  
TIENDA AM:PM  
LOCAL 133  
REPUBLICA DOMINICANA

CONTENIDO  
PLANTA ARQUITECTONICA  
DISTRIBUCION  
Y EQUIPAMIENTO

REVISION  
R46 / TERRAZA  
MODELO: R46  
REFERENCIA: R09

FECHA  
20 SEPTIEMBRE 2026

ESCALA  
1:40 / A2  
594 x 420 mm  
IMPRIMIR AL 100%

DOCUMENTACION  
ANTEPROYECTO  
VERIFICAR EN SITIO

LAMINA  
A-01