

Vista general

Distribución de la tienda · República Dominicana



Panorámica desde la entrada

Vista de acceso hacia las áreas comerciales y el fondo de la tienda.



Góndolas y pasillos

Exhibición central, cabeceras de producto y circulación comercial.



Licores

Mueble con divisiones, identidad AM:PM y marco con acabado tipo ladrillo.



Bebidas y Beer Cave

Frente refrigerado y acceso al Beer Cave desde el área de ventas.



Food Service

Nachos, grill, repostería y bebidas, con menú en dos pantallas.



Cajas y servicios

Dos cajas de venta y Mi Ban-kito, con pantallas orientadas al cliente.



Café, panadería y refrigerado


Café de autoservicio, panadería y alimentos listos para llevar.



Terraza

Terraza de 25,05 m² con siete mesas compactas y centros de mesa.



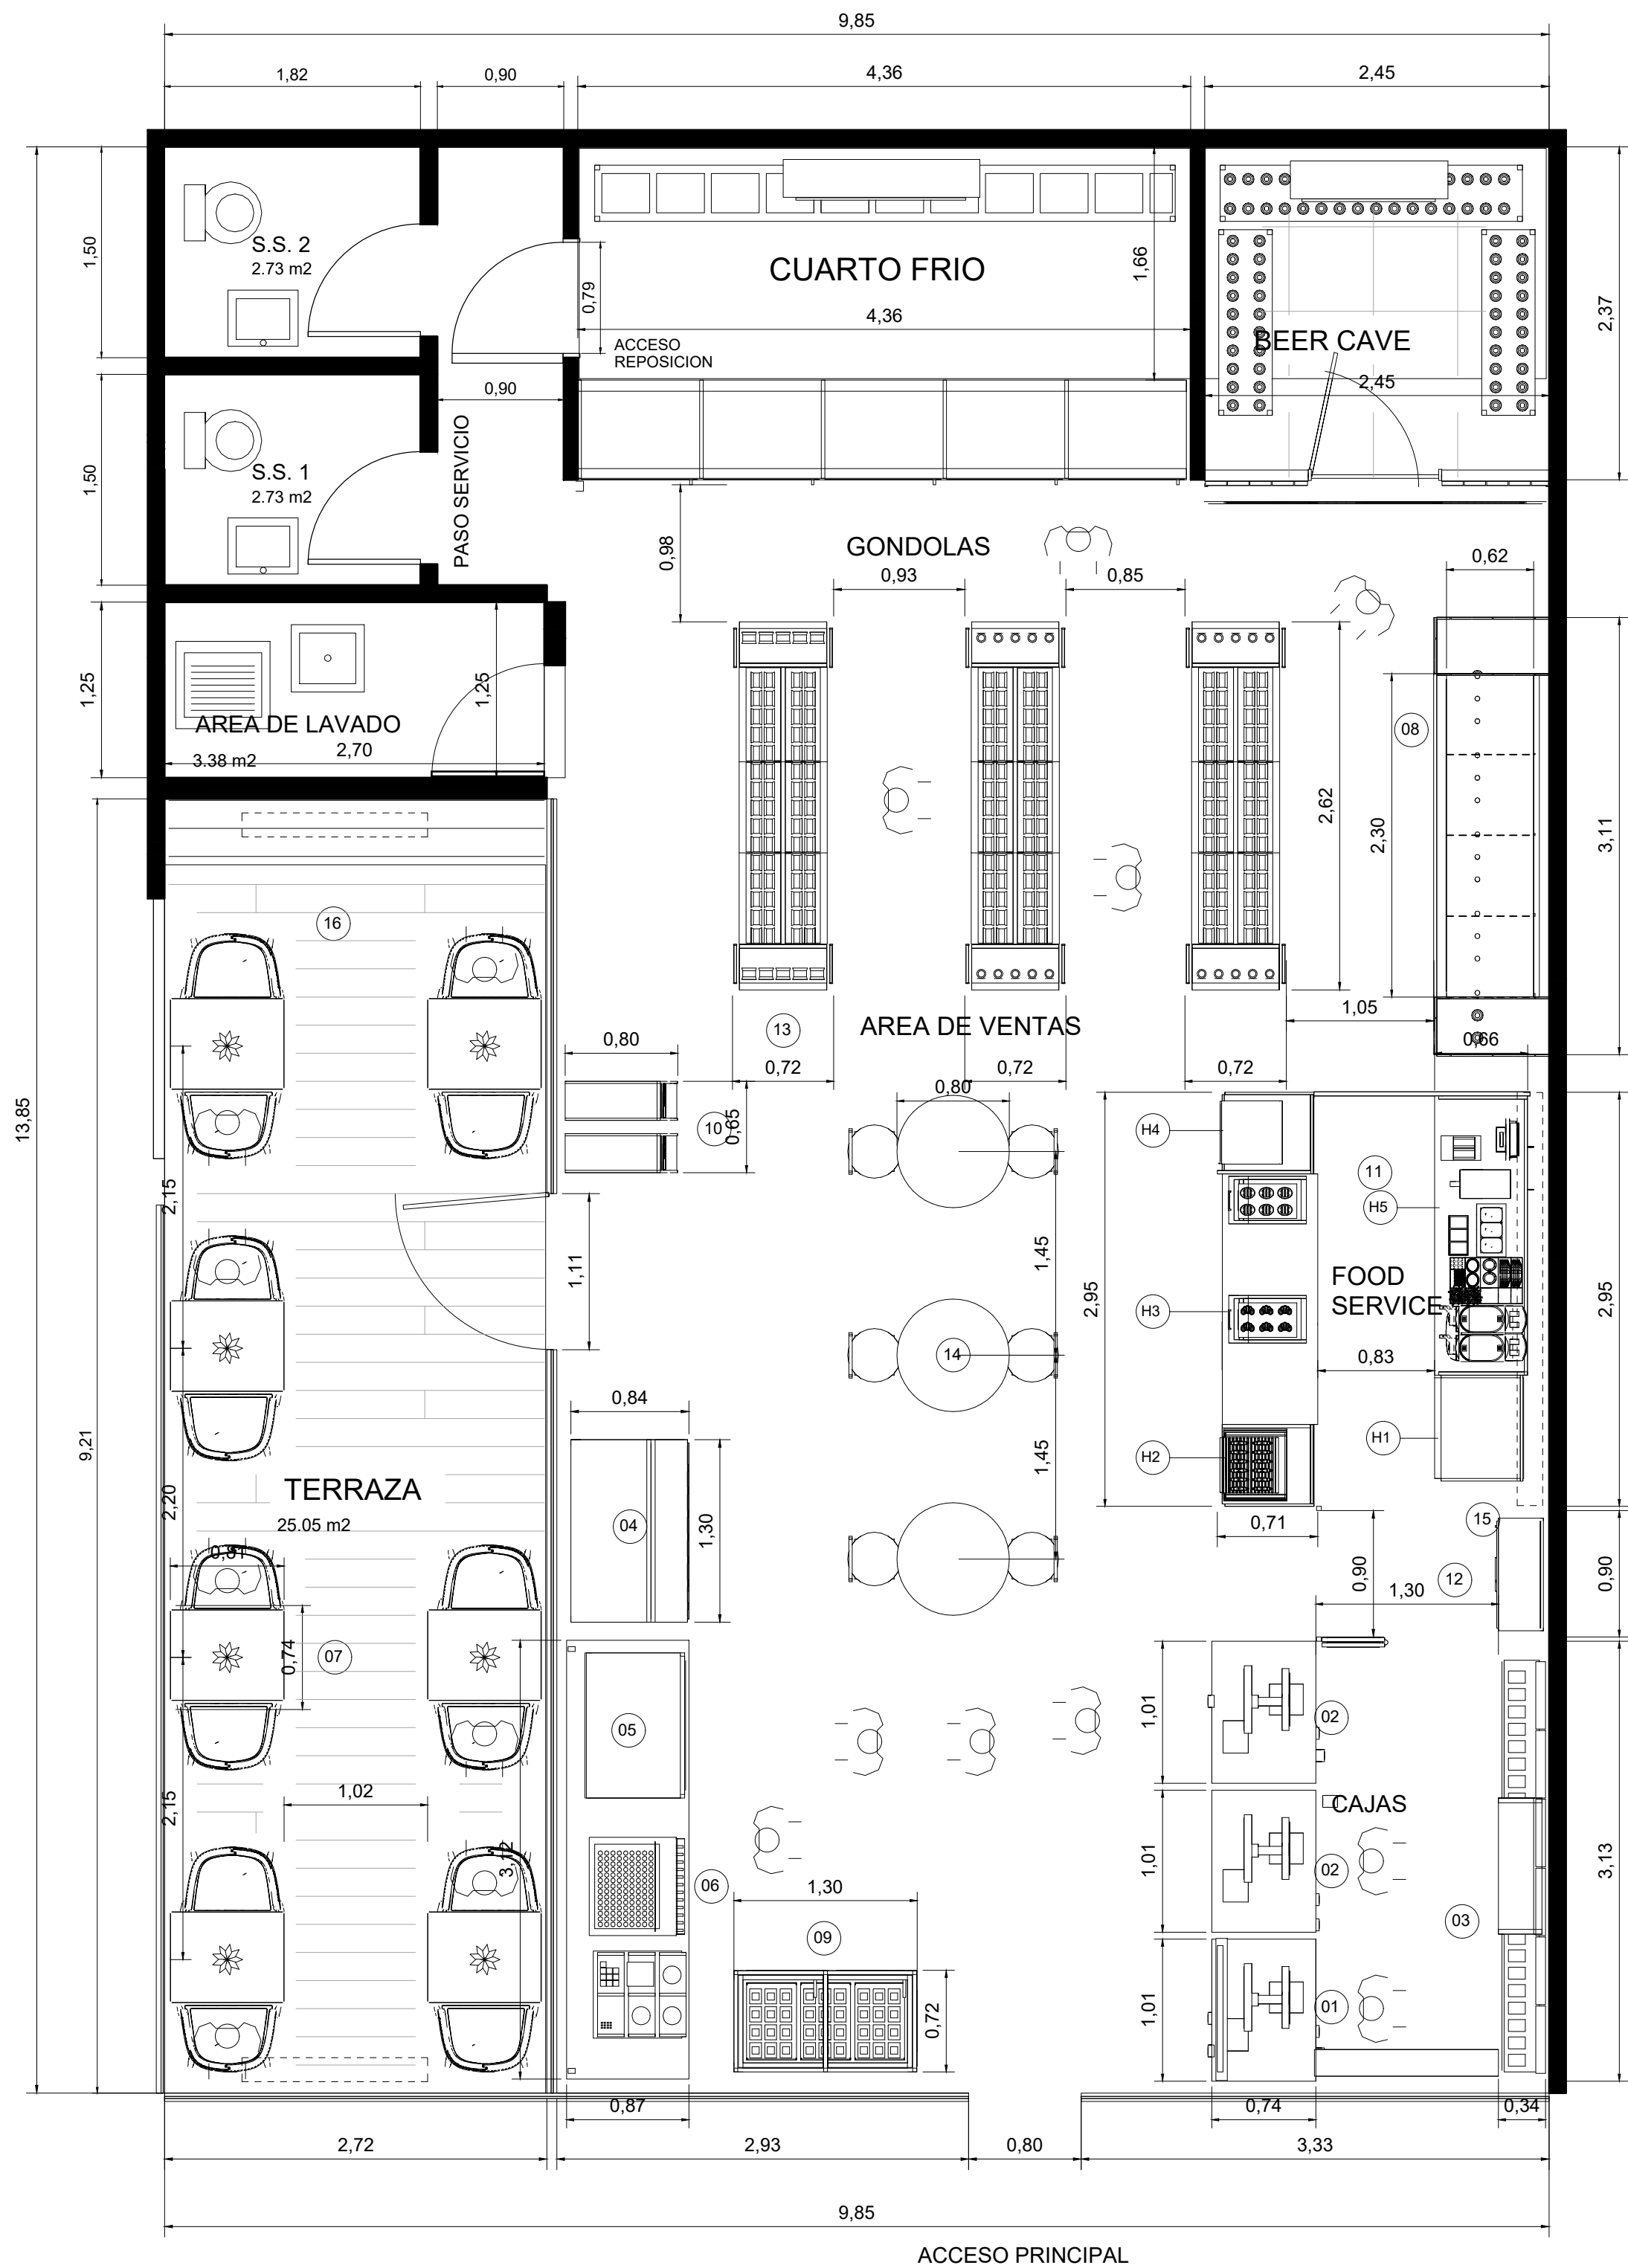

SIMBOLOGIA CONSTRUCTIVA

- Muros y tabiques en corte
- Mobiliario y equipamiento
- Vidrio / cerramiento ligero

Pisos: terraza / Beer Cave. Figuras humanas: escala y uso.

CUADRO DE EQUIPAMIENTO

CLAVE	DESCRIPCION	CANT.
01	Caja Mi Ban-kito / pagos y servicios	1
02	Caja normal con exhibicion de productos	2
03	Backwall / modulo central de cigarros	1
04	Matahambritas: 1.30 x 0.84 x 2.20 m	1
05	Vitrina de panaderia: frente 1.032 m	1
06	Cafetera + organizador de vasos	1
07	Mesa compacta 0.81 x 0.74 m / terraza	7
08	Mueble de licores / marco tipo ladrillo	1
09	Paletero horizontal Helados Bon	1
10	Cajero automatico ATM	1
11	Food Service: grill + 2 vitrinas acrilicas	1
12	Vitrina de electronica con vidrio	1
13	Gondolas centrales: 0.72 x 2.62 m	3
14	Mesa circular / alineada en area central	3
15	Pantallas 55 pulgadas / Food Service	2
16	Pantallas para ambiente musical / terraza	2

CUADRO DE SUPERFICIES / m2


SECTOR	MEDIDAS / m	m2
Tienda y circulaciones (*)	Por diferencia	86,40
Banos (2)	2 x 1.82 x 1.50	5,46
Terraza	2.72 x 9.21	25,05
Area de lavado	2.70 x 1.25	3,38
Cuarto frio	4.36 x 2.37	10,33
Beer Cave	2.45 x 2.37	5,81

TOTAL INTERIOR DEL LOCAL 9.85 x 13.85 136,42

(*) Incluye tabiques y pasos. No equivale a area util libre.
Areas nominales del modelo; sin deducir muebles. Verificar en sitio.
Paso 0.90 m con puerta fria cerrada; apertura hacia afuera.


D01 / LICORES - PLANTA DE MODULACION 1:20

Divisiones bajo repisa superior: linea discontinua en planta.

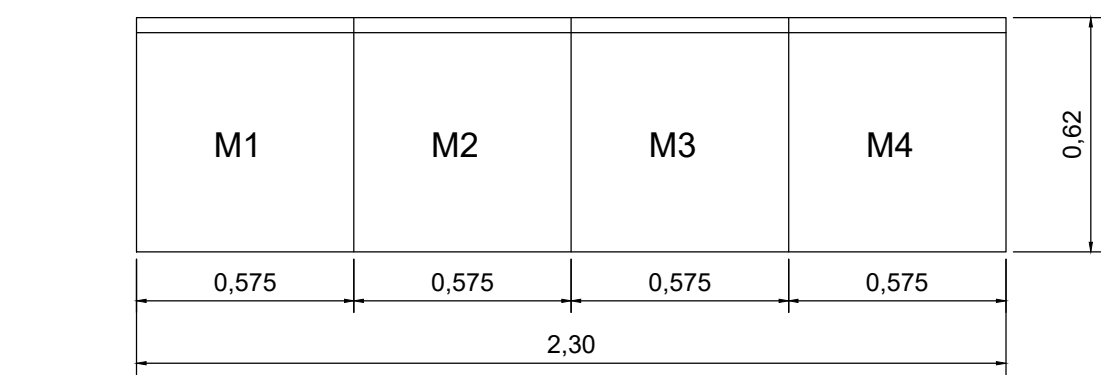

4 modulos nominales de 0.575 m / frente total 2.30 m.
Fondo de repisas 0.62 m. Remates exteriores: 3.11 m total.
Cotas del modelo. Espesores y medidas finales: verificar en sitio.

ESCALA GRAFICA / METROS

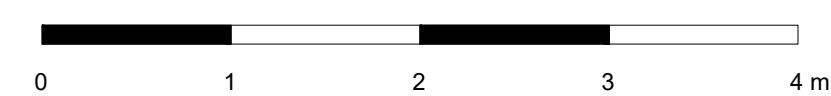

PLANTA ARQUITECTONICA
TIENDA AM:PM / LOCAL 133



PROYECTO
TIENDA AM:PM
LOCAL 133
REPUBLICA DOMINICANA

CONTENIDO
PLANTA ARQUITECTONICA
DISTRIBUCION
Y EQUIPAMIENTO

REVISION
R46 / TERRAZA
MODELO: R46
REFERENCIA: R09

FECHA
20 SEPTIEMBRE 2026

ESCALA
1:40 / A2
594 x 420 mm
IMPRIMIR AL 100%

DOCUMENTACION
ANTEPROYECTO
VERIFICAR EN SITIO

LAMINA
A-01